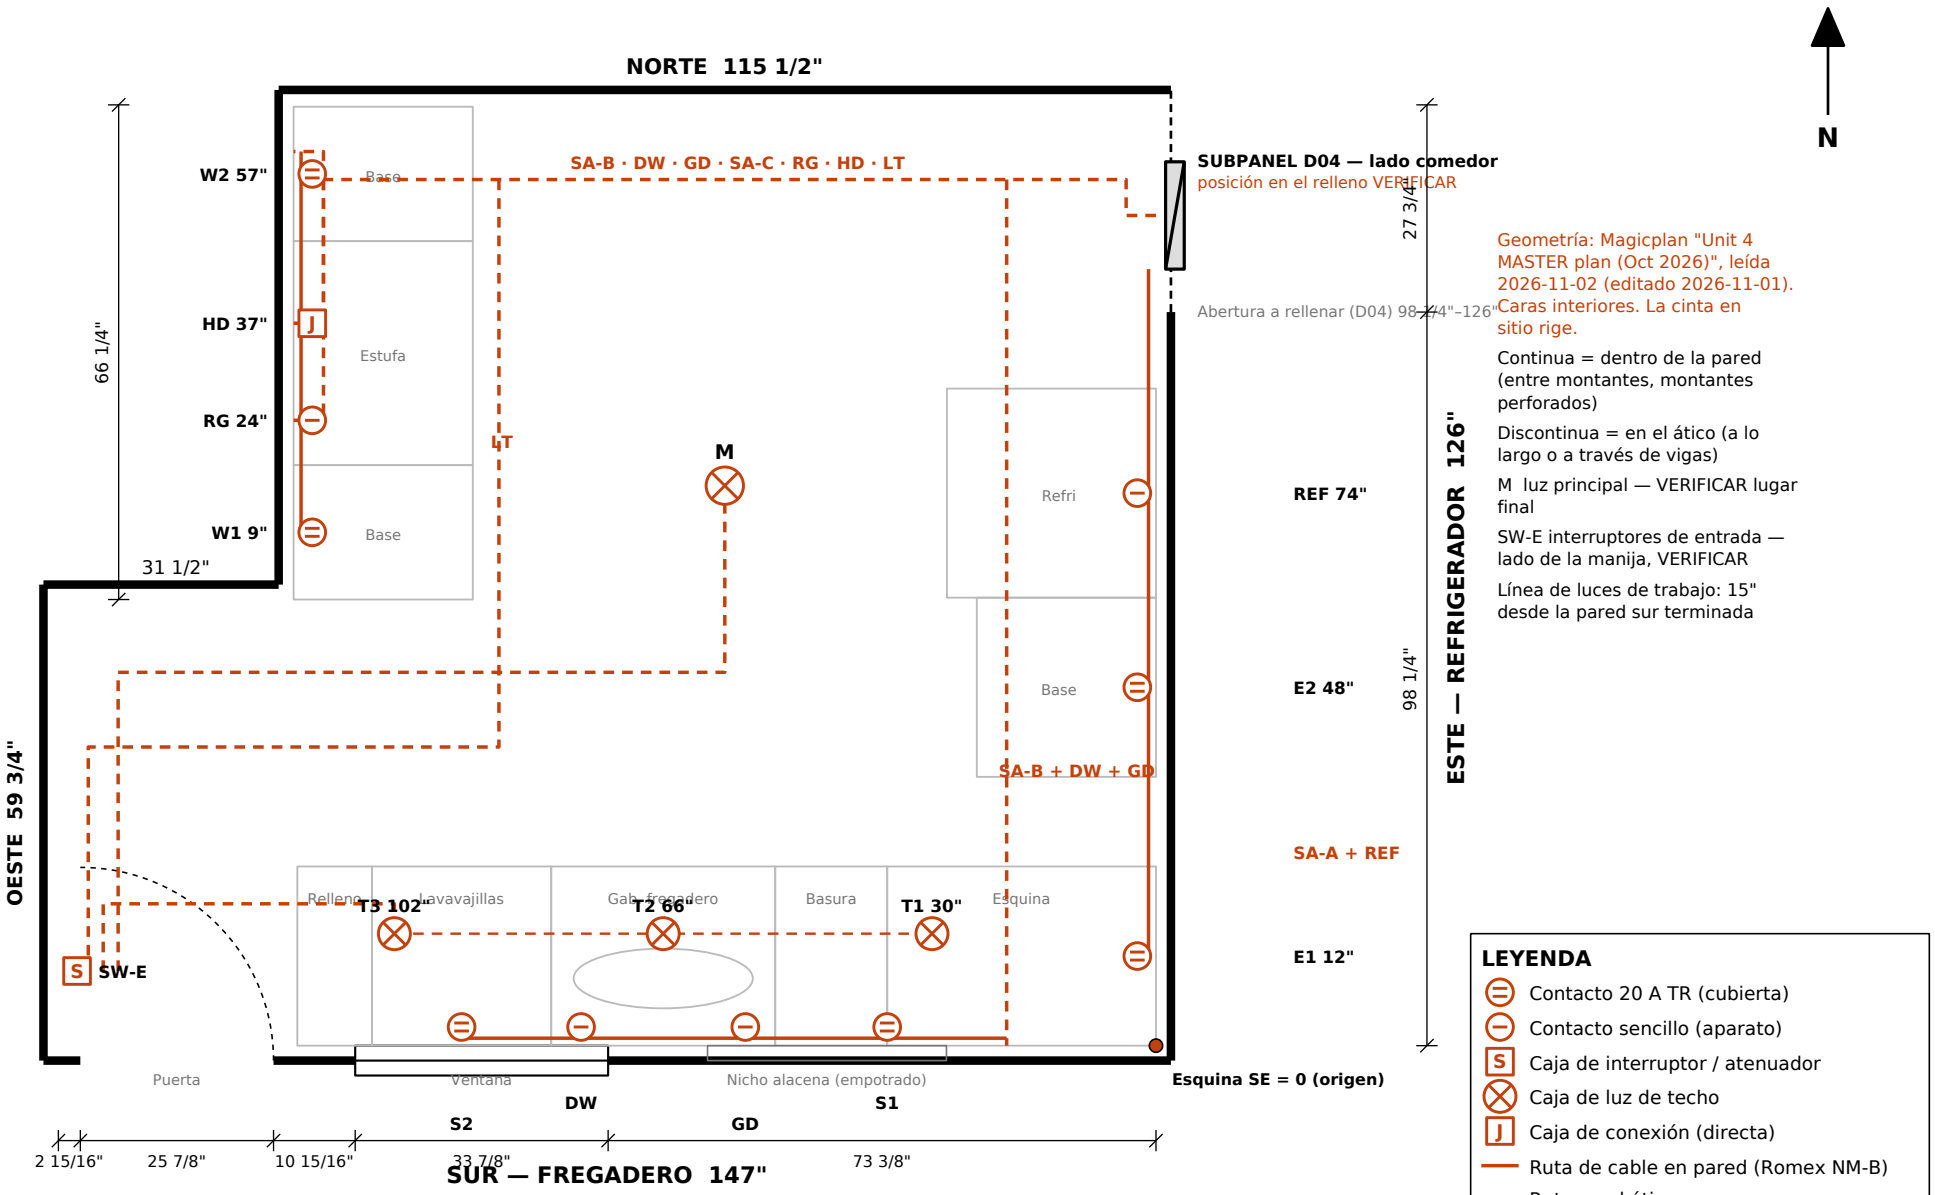


Geometría: Magicplan "Unit 4 MASTER plan (Oct 2026)", leída 2026-11-02 (editado 2026-11-01). Caras interiores. La cinta en sitio rige.

Continua = dentro de la pared (entre montantes, montantes perforados)

Discontinua = en el ático (a lo largo o a través de vigas)

M luz principal — VERIFICAR lugar final

SW-E interruptores de entrada — lado de la manija, VERIFICAR

Línea de luces de trabajo: 15" desde la pared sur terminada

LEYENDA

- Contacto 20 A TR (cubierta)
- Contacto sencillo (aparato)
- S Caja de interruptor / atenuador
- Caja de luz de techo
- J Caja de conexión (directa)
- Ruta de cable en pared (Romex NM-B)
- Ruta en el ático

Escala 1" = 2'-0" (1:24) en tamaño carta

0 4'

KE-01 Planta de cocina — dispositivos y rutas de cable

Edición en español. La edición en inglés es un archivo separado; el inglés rige.


BORRADOR — PLAN DE TRABAJO. VERIFICAR EN SITIO. No es juego de permiso ni liberación de instalación.

1231 11th Ave, Unidad 4 — San Francisco CA 94122 · Planos eléctricos de trabajo — cocina · Rev B · 2026-11-02 · reemplaza Rev A (misma fecha)

Rev B: cuarto a escala desde Magicplan; ventana, nicho, puerta y abertura ubicados; S1/S2 bajados a 40" AFF; bajada sur a la esquina; sin caja de interruptor en el fregadero.

Mirando al SUR. Esquina SE a la IZQUIERDA. Distancias desde la esquina SE (cara terminada).

Marca en subpiso = AFF + t (t = espesor del piso terminado, AÚN NO SE SABE)

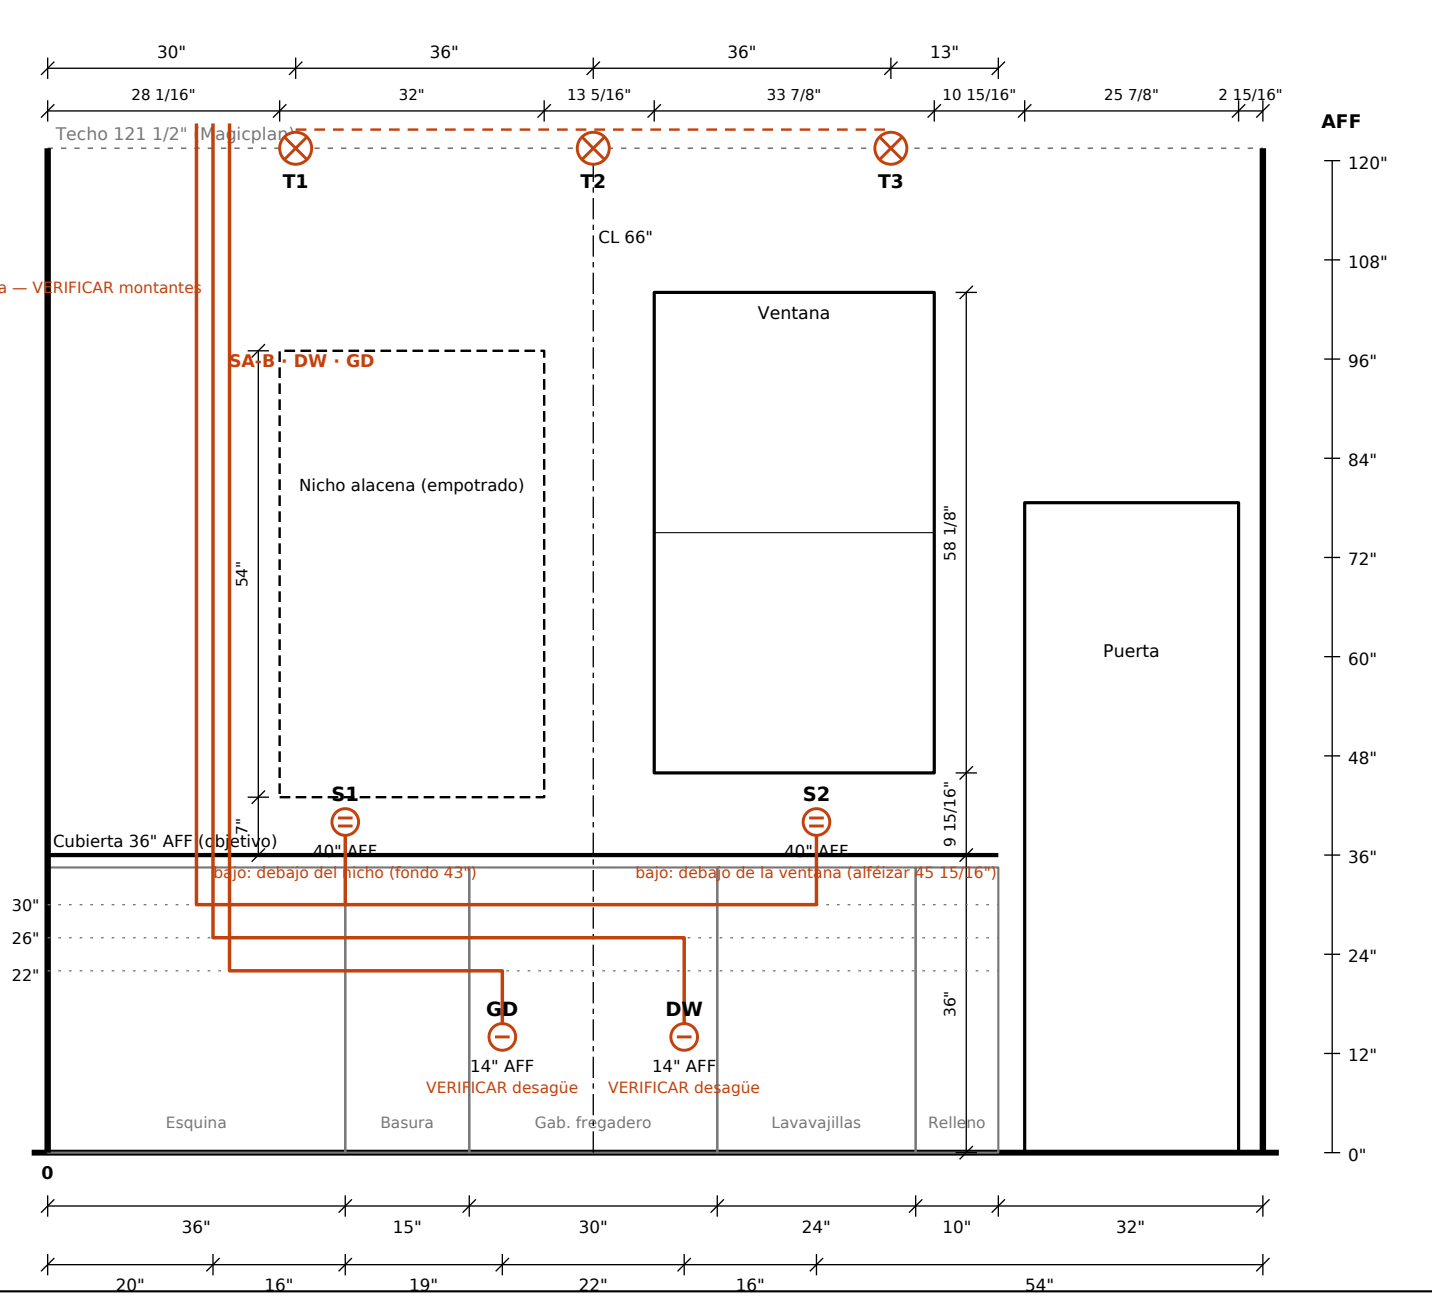

Escala 1/4" = 1'-0" (aprox. 1:48) en tamaño carta

0 2'

LUCES DE TRABAJO — 3 luminarias, separación igual de 36", la del centro en el eje del fregadero

T1 30" · T2 66" (CL) · T3 102"

Línea de luces de trabajo: 15" desde la pared sur terminada

Colgante o de techo. Si es colgante: máx. 10" de diámetro, parte baja 30–32" sobre la cubierta. La dueña decide 3 o las 2 anteriores.

Control de luces junto al fregadero: control inalámbrico (p. ej. Lutron Pico) — sin caja ni cable. Triturador: interruptor neumático en la cubierta (sin caja) o interruptor de pared — la dueña elige.

LEYENDA

- Contacto 20 A TR (cubierta)
- Contacto sencillo (aparato)
- Caja de interruptor / atenuador
- Caja de luz de techo
- Caja de conexión (directa)
- Ruta de cable en pared (Romex NM-B)
- Ruta en el ático

KE-02 Pared sur (fregadero) — dispositivos, rutas, luces de trabajo

Edición en español. La edición en inglés es un archivo separado; el inglés rige.

BORRADOR — PLAN DE TRABAJO. VERIFICAR EN SITIO. No es juego de permiso ni liberación de instalación.

1231 11th Ave, Unidad 4 — San Francisco CA 94122 · Planos eléctricos de trabajo — cocina · Rev B · 2026-11-02 · reemplaza Rev A (misma fecha)


Rev B: cuarto a escala desde Magicplan; ventana, nicho, puerta y abertura ubicados; S1/S2 bajados a 40" AFF; bajada sur a la esquina; sin caja de interruptor en el fregadero.

Mirando al ESTE. Esquina SE a la DERECHA. Distancias desde la esquina SE, hacia el norte.

Marca en subpiso = AFF + t (t = espesor del piso terminado, AÚN NO SE SABE)

Escala 1/4" = 1'-0" (aprox. 1:48) en tamaño carta

0 2'

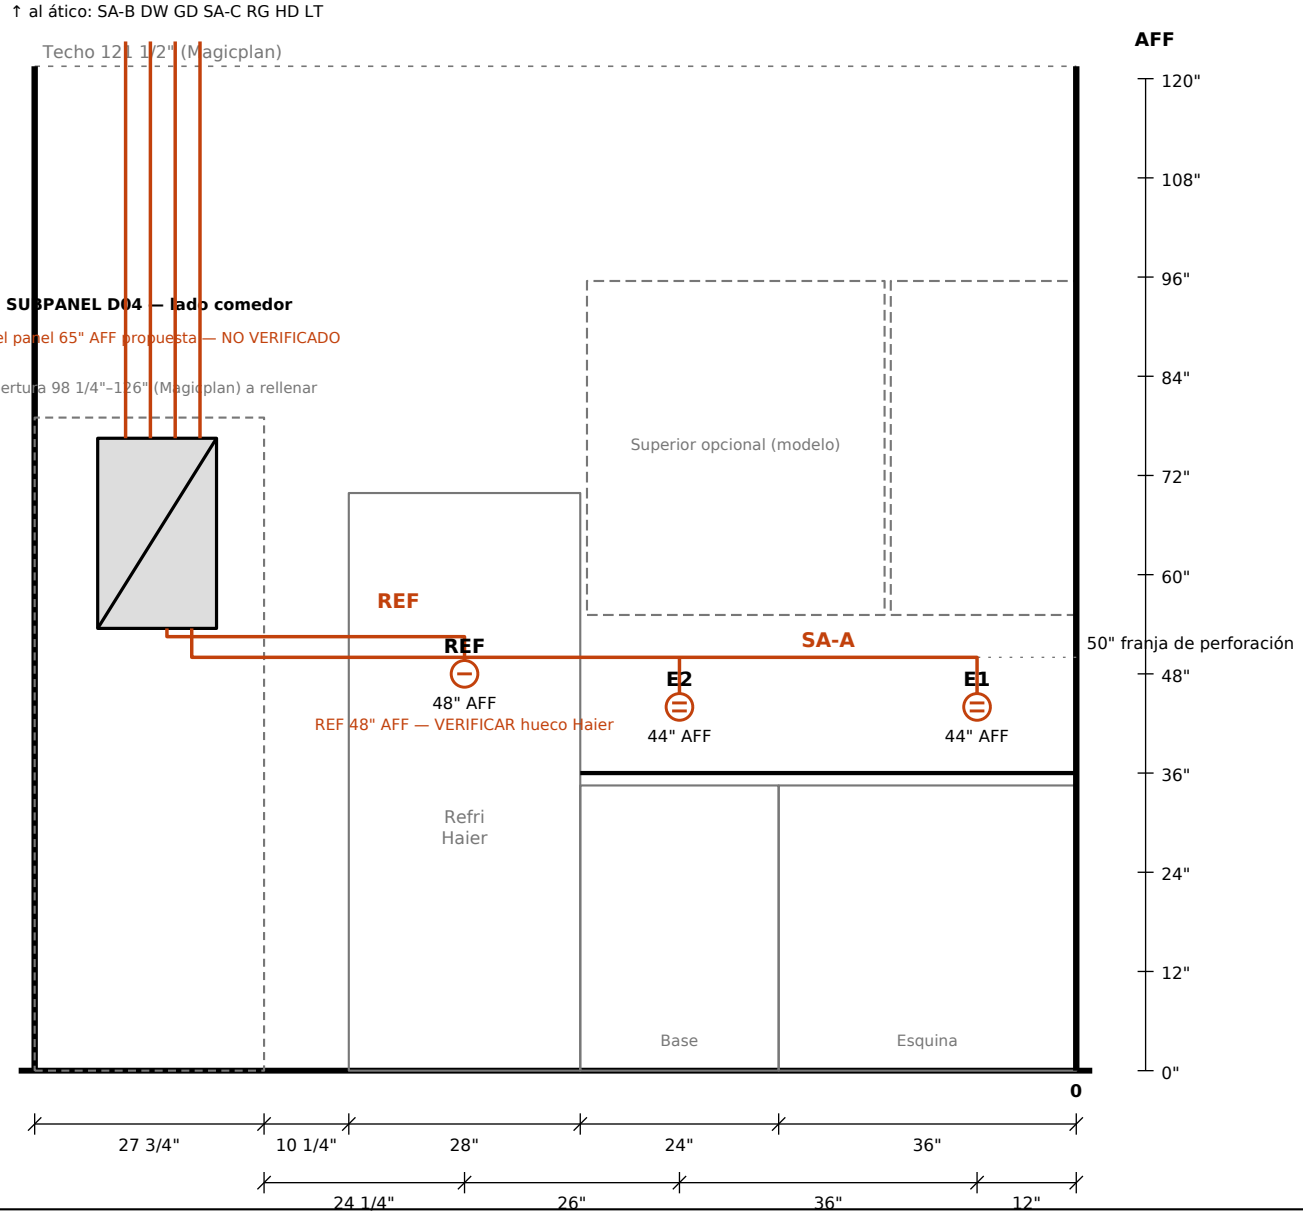

LEYENDA

- Contacto 20 A TR (cubierta)
- Contacto sencillo (aparato)
- Caja de interruptor / atenuador
- Caja de luz de techo
- Caja de conexión (directa)
- Ruta de cable en pared (Romex NM-B)
- Ruta en el ático

KE-03 Pared este (refrigerador) — dispositivos y rutas

Edición en español. La edición en inglés es un archivo separado; el inglés rige.

BORRADOR — PLAN DE TRABAJO. VERIFICAR EN SITIO. No es juego de permiso ni liberación de instalación.

1231 11th Ave, Unidad 4 — San Francisco CA 94122 · Planos eléctricos de trabajo — cocina · Rev B · 2026-11-02 · reemplaza Rev A (misma fecha)

Rev B: cuarto a escala desde Magicplan; ventana, nicho, puerta y abertura ubicados; S1/S2 bajados a 40" AFF; bajada sur a la esquina; sin caja de interruptor en el fregadero.


Mirando al OESTE, pared de estufa. Extremo sur (esquina exterior) a la IZQUIERDA. Distancias desde esa esquina, hacia el norte.

Marca en subpiso = AFF + t (t = espesor del piso terminado, AÚN NO SE SABE)

Escala 1/4" = 1'-0" (aprox. 1:48) en tamaño carta

0 2'

En Magicplan la campana está a 35 11/16" de esta esquina; rige el eje de estufa de 33" del K002.

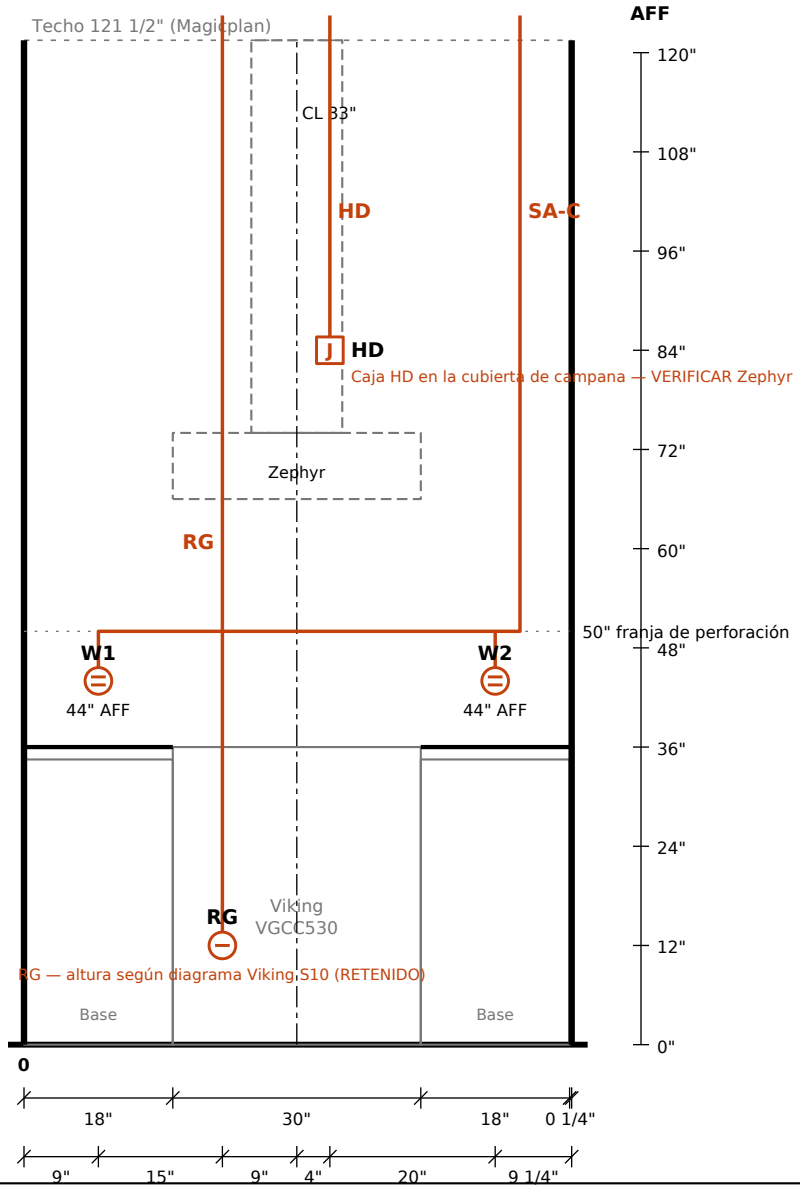

LEYENDA

- Contacto 20 A TR (cubierta)
- Contacto sencillo (aparato)
- Caja de interruptor / atenuador
- Caja de luz de techo
- Caja de conexión (directa)
- Ruta de cable en pared (Romex NM-B)
- Ruta en el ático

KE-04 Pared oeste (estufa) — dispositivos y rutas

Edición en español. La edición en inglés es un archivo separado; el inglés rige.

BORRADOR — PLAN DE TRABAJO. VERIFICAR EN SITIO. No es juego de permiso ni liberación de instalación.

1231 11th Ave, Unidad 4 — San Francisco CA 94122 · Planos eléctricos de trabajo — cocina · Rev B · 2026-11-02 · reemplaza Rev A (misma fecha)

Rev B: cuarto a escala desde Magicplan; ventana, nicho, puerta y abertura ubicados; S1/S2 bajados a 40" AFF; bajada sur a la esquina; sin caja de interruptor en el fregadero.

CÓMO SE TIENDE EL CABLE — sin diagonales

1. Dentro de paredes: lo vertical se queda en un solo espacio entre montantes; lo horizontal va derecho por agujeros perforados a una altura fija.
2. Perforar al centro del montante. Si el borde del agujero queda a menos de 1-1/4" de la cara, poner placa de acero (300.4(A)).
3. Por soleras superior e inferior: perforar y sellar el agujero con sellador o espuma resistente al fuego (cortafuego).
4. Ático: correr al costado de las vigas o por agujeros perforados. Encima de las vigas a menos de 6 ft de la escotilla: tiras de protección obligatorias.
5. Grapar a menos de 12" de cada caja y al menos cada 4-1/2 ft. No más de 2 cables por agujero salvo que el electricista reduzca capacidad.
6. Las franjas evitan los tornillos de gabinetes: pared este y de estufa 50" AFF (superiores desde 55"); sur 30" (SA-B), 26" (lavavajillas), 22" (triturador) detrás de las bases.
7. Pared sur: ningún cable por el nicho, el cabezal de la ventana ni el respiradero del fregadero. Todos los cables del sur bajan en el espacio de la esquina (unas 20" desde SE), a la izquierda del nicho.
8. Dejar cables y cajas abiertos hasta pasar la inspección en bruto (contratista con licencia, permiso de SF).

PENDIENTES ANTES DE MARCAR

S1/S2 a 40" AFF es propuesta (la dueña decide): S1 queda debajo del nicho, S2 debajo de la ventana.
K-E02 Profundidad de la moldura del alféizar no registrada — la parte alta de la caja S2 debe librarla.
K-E03 Método GFCI de la estufa (breaker DF o GFCI sin contacto) — electricista.
K-E04 Capacidad y posición de caja de la campana Zephyr — leer placa o manual actual.
K-E07 Espesor del piso t desconocido — toda marca en subpiso = AFF + t.
Los montantes no están levantados. Los espacios de bajada son objetivo; el electricista usa el más cercano.
La posición del panel D04 dentro del relleno y su altura no están verificadas (primero caja y tapa en mano).

TABLA DE MARCAS — centros de caja

Marca	Pared	Desde origen	AFF	Circuito	Nota
E1	Este	12"	44"	SA-A	
E2	Este	48"	44"	SA-A	
REF	Este	74"	48"	REF	VERIFICAR hueco Haier
S1	Sur	36"	40"	SA-B	debajo del nicho
GD	Sur	55"	14"	GD	
DW	Sur	77"	14"	DW	
S2	Sur	93"	40"	SA-B	debajo de ventana, VERIF. moldura
W1	Estufa	9"	44"	SA-C	
RG	Estufa	24"	—	RG	Viking S10 (RETENIDO)
HD	Estufa	37"	—	HD	VERIFICAR Zephyr
W2	Estufa	57"	44"	SA-C	
SW-E	Oeste	10"	48"	LT	desde esquina SO, VERIFICAR
T1	Techo	30"	—	LT	15" desde pared sur
T2	Techo	66"	—	LT	15" desde pared sur
T3	Techo	102"	—	LT	15" desde pared sur
M	Techo	(57.75", 75")	—	LT	VERIFICAR lugar

Marca en subpiso = AFF + t (t = espesor del piso terminado, AÚN NO SE SABE)

CIRCUITOS — D04 Eaton BRP20L125G

SA-A	20 A	12/2	DF	E1, E2
SA-B	20 A	12/2	DF	S1, S2
SA-C	20 A	12/2	DF	W1, W2
REF	20 A	12/2	DF	Refrigerador
DW	15 A	14/2	DF	Lavavajillas
GD	15 A	14/2	DF	Triturador
RG	15 A	14/2	K-E03	Estufa Viking
HD	15 A	14/2	AFCI	Campana Zephyr
LT	15 A	14/2 (+14/3 solo si es 3 vías)	AFCI	Luces

LEYENDA

- Contacto 20 A TR (cubierta)
- Contacto sencillo (aparato)
- S — Caja de interruptor / atenuador
- Caja de luz de techo
- J — Caja de conexión (directa)
- Ruta de cable en pared (Romex NM-B)
- Ruta en el ático

KE-05 Reglas de cableado, leyenda, tabla de marcas

Edición en español. La edición en inglés es un archivo separado; el inglés rige.

BORRADOR — PLAN DE TRABAJO. VERIFICAR EN SITIO. No es juego de permiso ni liberación de instalación.

1231 11th Ave, Unidad 4 — San Francisco CA 94122 · Planos eléctricos de trabajo — cocina · Rev B · 2026-11-02 · reemplaza Rev A (misma fecha)

Rev B: cuarto a escala desde Magicplan; ventana, nicho, puerta y abertura ubicados; S1/S2 bajados a 40" AFF; bajada sur a la esquina; sin caja de interruptor en el fregadero.